


ESQUEMA DE LOCALIZACION

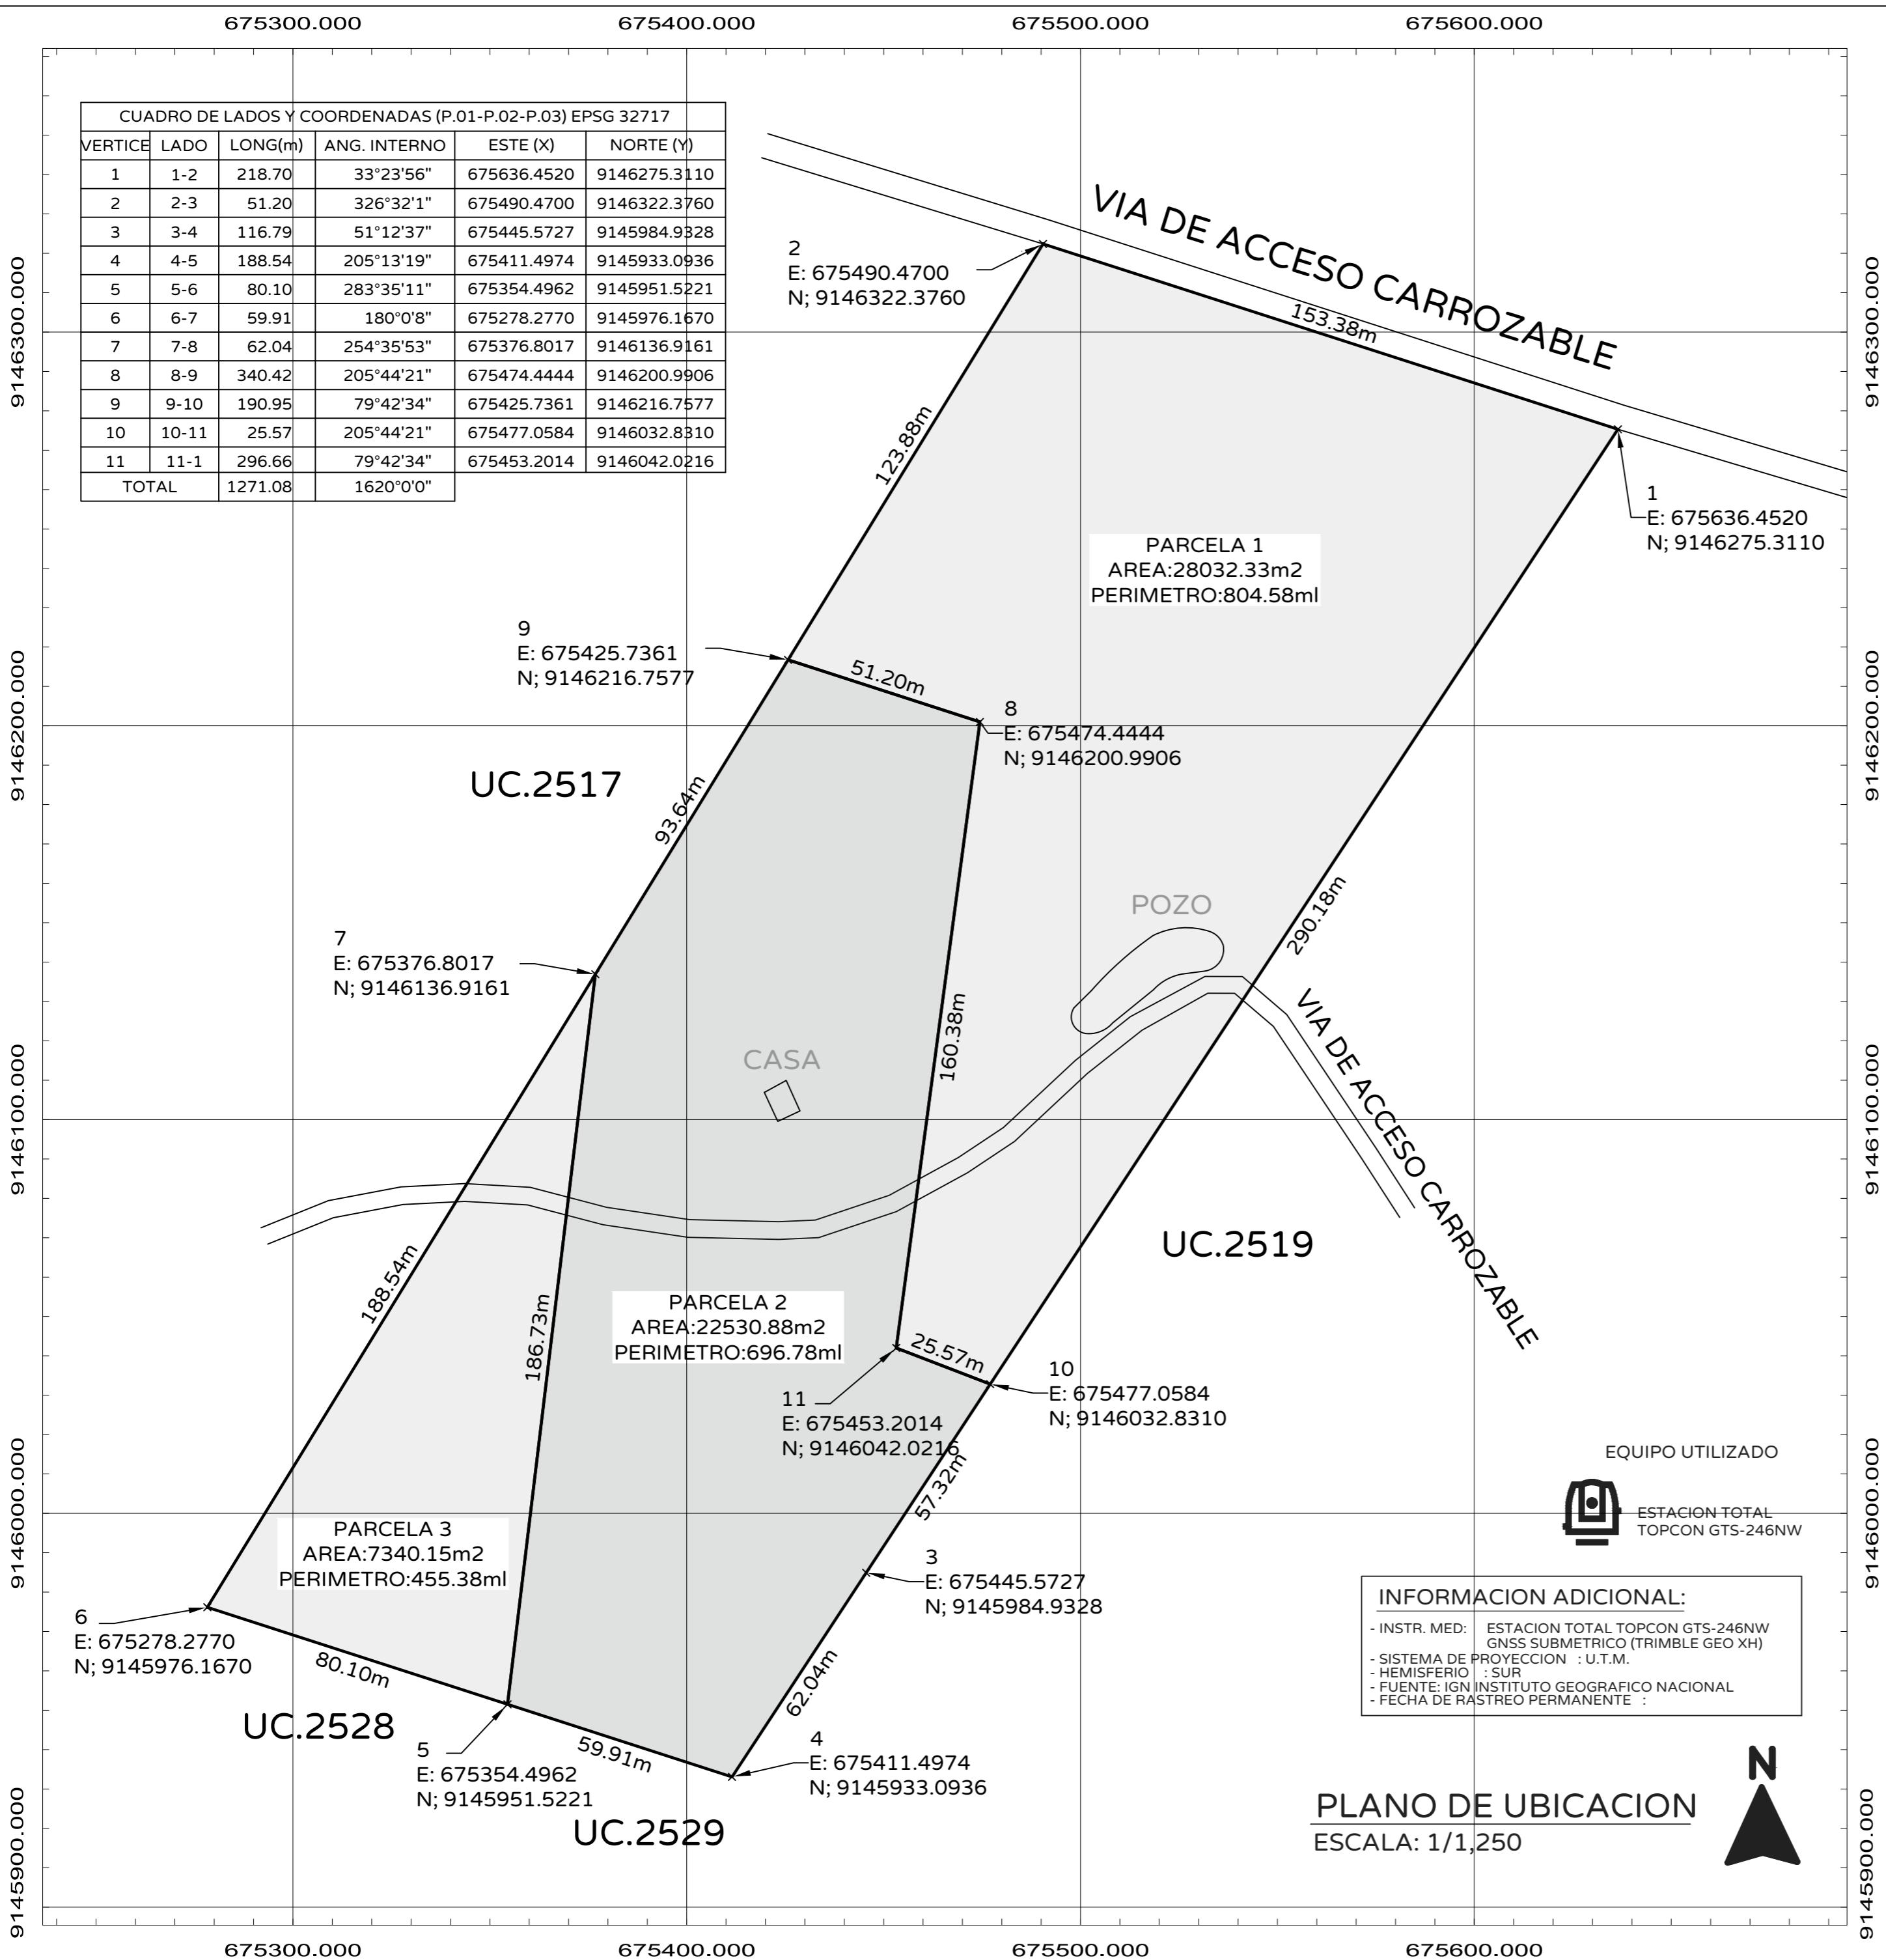

CUADRO DE TRAMOS Y COLINDANCIAS - PARCELA 02			
TRAMO	LONG(m)	COLINDANCIA	ORIENT.
7-9	93.64	UC.2517	OESTE
9-8	51.20	PARCELA 01	NORTE
8-11	160.38	PARCELA 01	ESTE
11-10	25.57	PARCELA 01	ESTE
10-3	57.32	UC.2519	ESTE
3-4	62.04	UC.2519	ESTE
4-5	59.91	UC.2529	SUR
5-7	186.73	PARCELA 03	OESTE

DATOS INFORMATIVOS DEL PREDIO RUSTICO		
ADMINISTRADA:	GINA YSABEL RUIZ JAUREGUI	AREA Y PERIMETRO
		AREA: INDICADA
DEPARTAMENTO:	LA LIBERTAD	PERIMETRO: INDICADO
PROVINCIA:	ASCOPE	MOD.CALC:CASTESIANO
DISTRITO:	RAZURI	DATUM: WGS-84
SECTOR:	LA PAMPA	ZONA: 17 S
NOMBRE PREDIO:	POLIGONO-2518	SISTEMA DE PROY: U.T.M

PROYECTO: **ADQUISICION DE PREDIO RUSTICO**

PLANO: **UBICACION Y LOCALIZACION**

ESCALA: **INDICADAS** FECHA: **FEBRERO-2026** LAMINA:

PROYECTISTA: **JEFFERSON ANAMPA VALDERRAMA**

FIRMA Y SELLO DEL PROFESIONAL: **U1**